
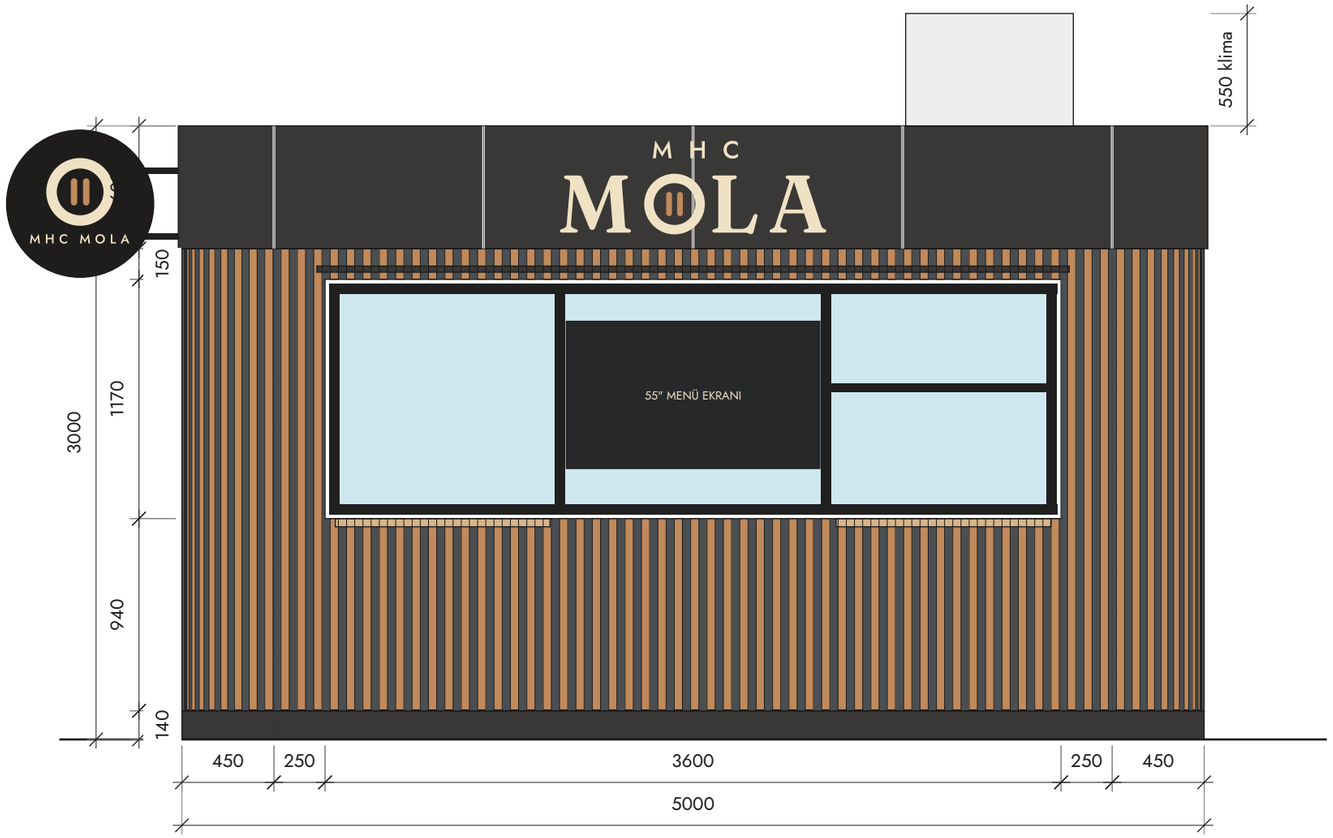



ÖNDEN GÖRÜNÜŞ (cam tarafı)

Ölçek 1:30

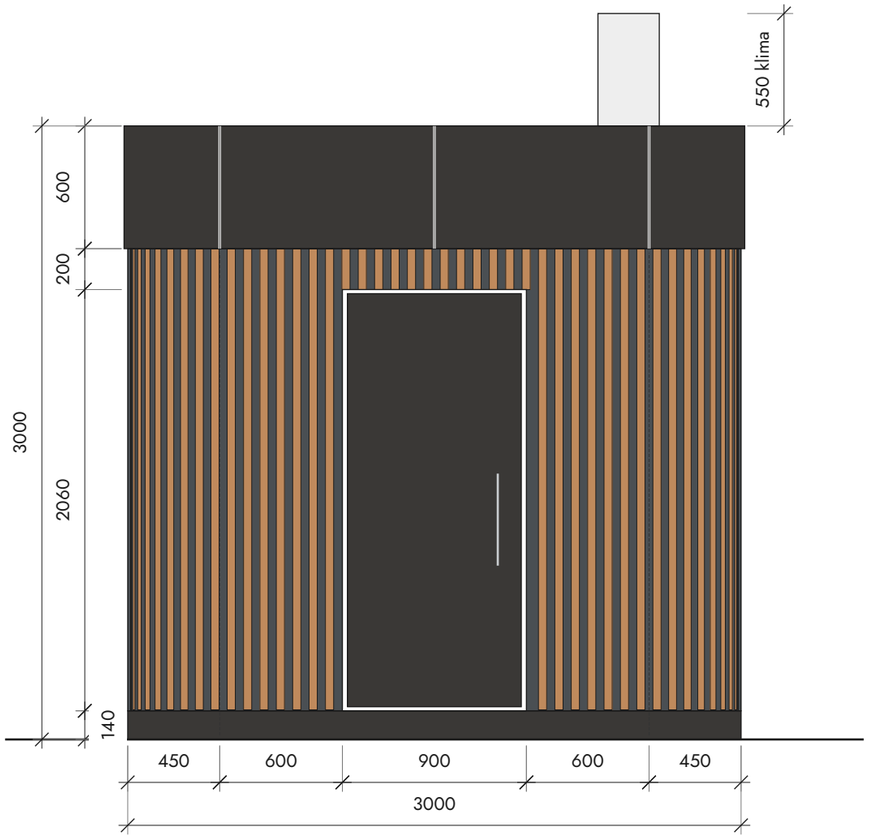

YANDAN GÖRÜNÜŞ (kapı tarafı)

Ölçek 1:30

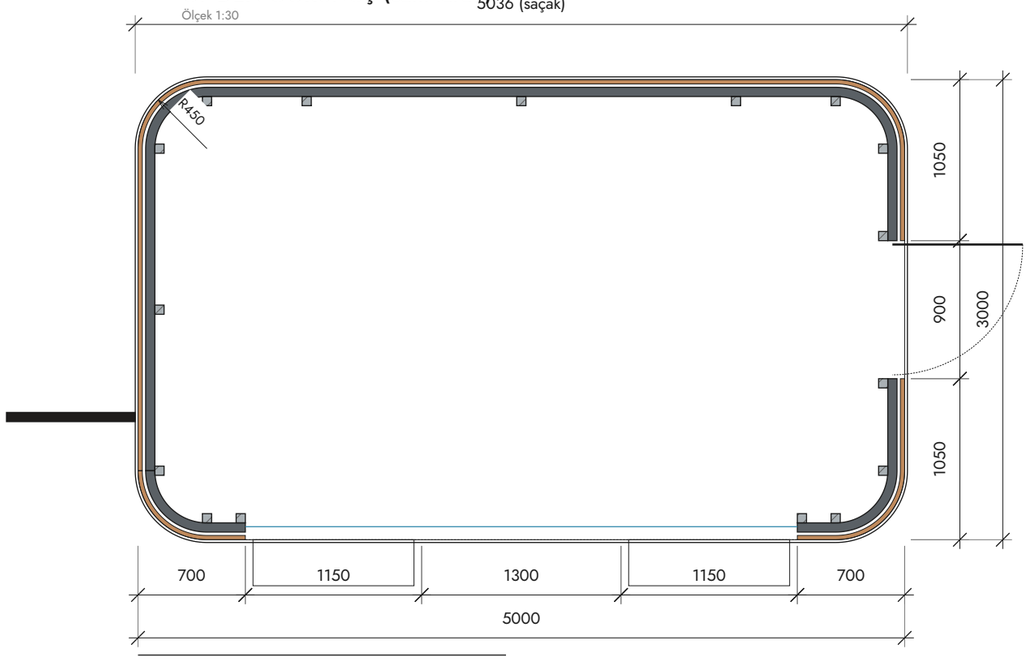

ÜSTTEN (plan)

Ölçek 1:40

ÖNEMLİ ÖLÇÜLER (mm)

Dış ölçü	5000 × 3000
Yükseklik	3000
Köşeler yuvarlak	R450
Ön cam (tam ortada)	3600 × 1170
Cam alt kenarı	+1080
Kapı (sağ yan)	900 × 2060
Üst siyah bant	600 yüksek
Alt siyah süpürgelik	140 yüksek
İç tavan	+2500
Klima boşluğu	+2500 … +2840

YAPIM SIRASI

1. Demir şasi (sayfa 2)
2. Sandviç panel giydir
3. Cam ve kapı boşluğunu kes
4. Siyah karkas + ahşap çıta
5. Üst banda alükobond
6. Cam, kapı, tavan, klima

Ölçüler milimetredir (mm).

Kotlar (+) şasinin altından ölçülür.

MHC Mola · Kiosk

5.0 × 3.0 × 3.0 m · prefabrik kahve kioskusu


GENEL ÖLÇÜLER

Tüm ölçüler mm'dir. Ölçüler sahada kontrol edilmeden imalata başlanmaz.

PAFTA 1/3

ÖLÇEK 1:30 · 1:40

TARİH 28.10.2026

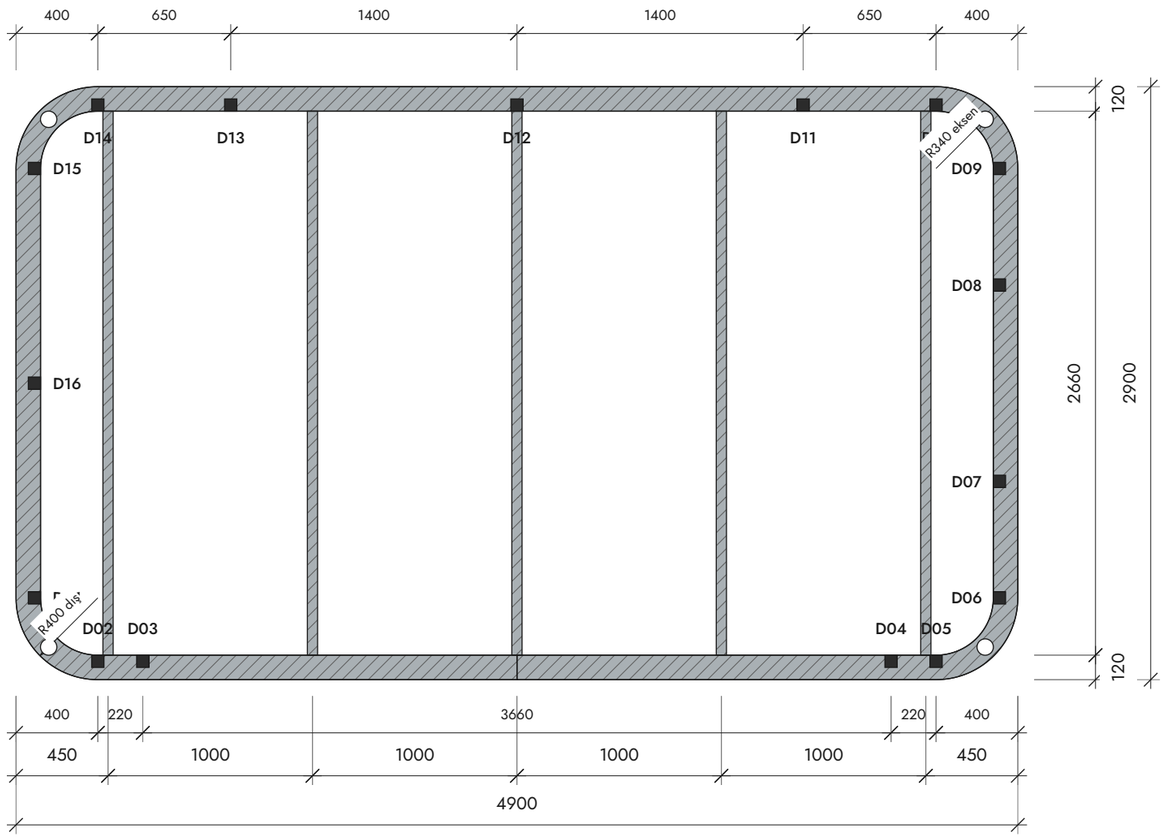

DEMİR LİSTESİ


Profil	Nerede	Boy × adet (mm)
120×120×4 kutu	Taban çerçeve	2 × 4100 + 2 × 2100 + 4 köşe yayı R340
100×50×3 kutu	Taban kirişi (her 1000)	5 × 2660
60×60×3 kutu	Dikme	16 × 2720
60×60×3 kutu	Üst çerçeve	2 × 4100 + 2 × 2100 + 4 köşe yayı R310
60×100×3 kutu	Cam altı / cam üstü / kapı üstü	1 × 3600 + 1 × 3600 + 1 × 900
40×20×2 kutu	Köşe kaburgası (bükülü)	8 × 518 (R330)
60×40×2 kutu	Çatı kirişi	3 × 4660
40×40×2 kutu	Asma tavan taşıyıcı	5 × 2660

DİKKAT

- Köşe dikmeleri radüsün başladığı yerde.
- Köşegen farkı en fazla 3 mm.
- Taban çerçevesi ve üst çerçeve köşelerde hadde ile bükülür (yarıçap yukarıda).
- Köşelere 4 adet ayarlı ayak + kaldırma kulağı.
- Tüm demir: galvaniz veya astar + antrasit boya.
- Profiller öneridir; mühendis kontrol etmeli.


ŞASİ ÜSTTEN (taban çerçeve + kirişler + dikmeler)

Ölçek 1:30

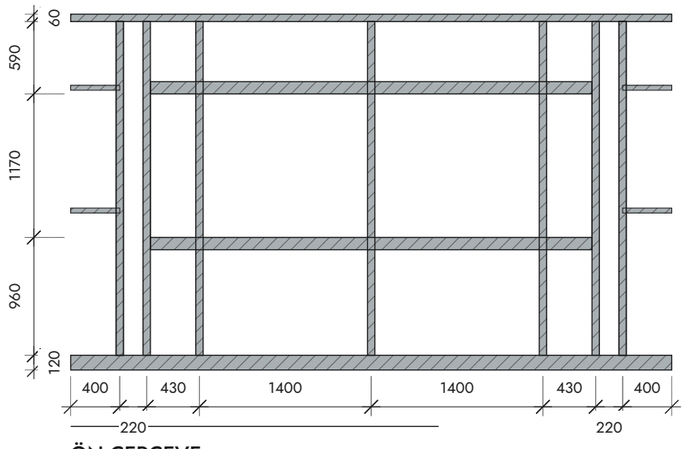

ÖN ÇERÇEVE

Ölçek 1:50

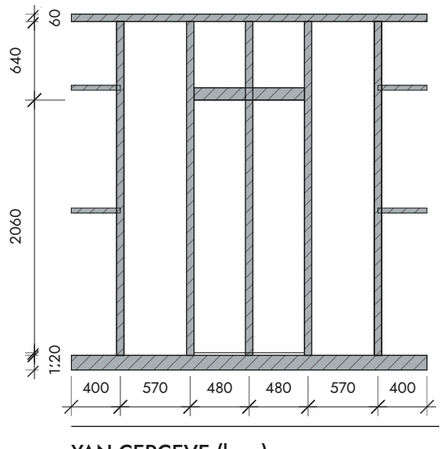

YAN ÇERÇEVE (kapı)

Ölçek 1:50

MHC Mola · Kiosk

5.0 × 3.0 × 3.0 m · prefabrik kahve kioskusu


DEMİR ŞASİ

Tüm ölçüler mm'dir. Ölçüler sahada kontrol edilmeden imalata başlanmaz.


PAFTA 2/3

ÖLÇEK 1:30 · 1:40

TARİH 28.10.2026

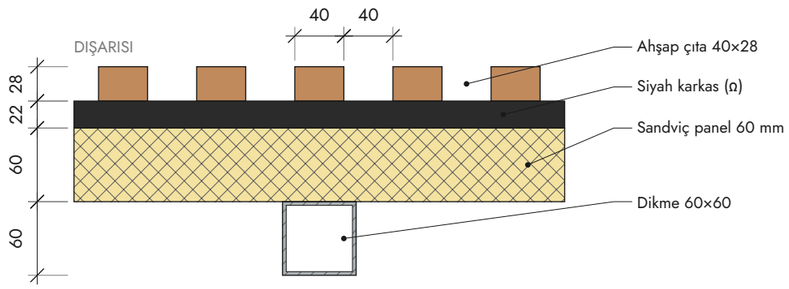

DUVAR KESİTİ (düz duvar)
Ölçek 1:5

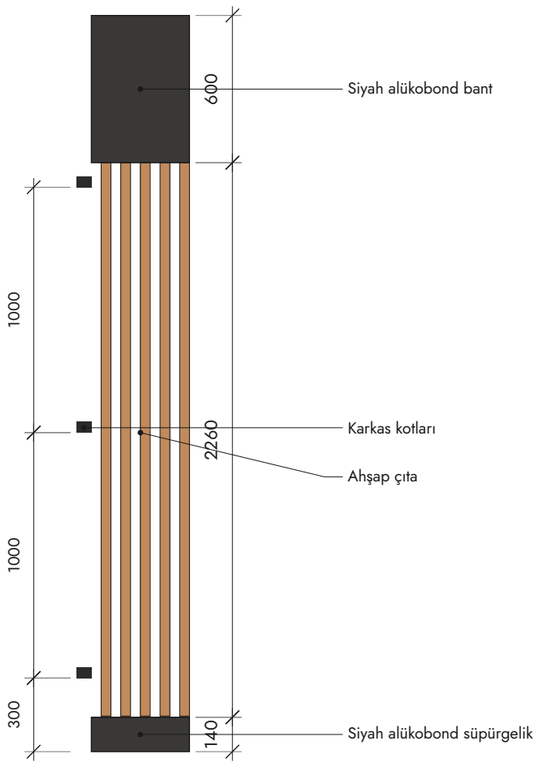

DUVAR DİZİLİMİ (aşağıdan yukarı)
Ölçek 1:25

SANDVİÇ PANEL 60 mm (dış antrasit, iç beyaz)

· Ön cephe: 2 × 247×2780, 1 × 3597×960, 1 × 3597×650
· Sağ cephe: 2 × 597×2780, 1 × 897×700
· Arka cephe: 4 × 1022×2780
· Sol cephe: 2 × 1047×2780
· 4 köşe: kavisli sac + taşyünü, dış R400, yükseklik 2780

AHŞAP ÇITA 40×28

· Aralık 40 mm (her 80 mm'de bir çıta), köşelerde de aynı.
· 133 adet 2255, 45 adet 935, 12 adet 200, 45 adet 150 mm.
· Her çıta, geçtiği her karkasa 2 paslanmaz vida.

SİYAH ALÜKOBOND (4 mm)

· Üst bant: 600 yüksek, 16 parça, aralarında 8 mm derz.
  12 düz parça (1017 / 1042 geniş), 4 köşe parçası (kavisli, 727).
· Bant, çıtanın 18 mm önünde durur.
· Alt süpürgelik: 140 yüksek, çepeçevre 15.3 m.
· Cam ve kapı kenarları da alükobond ile kaplanır.

CAM (6 mm temperli, siyah doğrama)

· Toplam boşluk 3600 × 1170, ön cephenin tam ortası.
· sipariş 1075×1050, ekran 1270×1050, teslim üst 1075×460, servis kapağı 1075×570.
· Sağ alttaki cam (servis kapağı) yukarı kayar.
· Ortadaki camın arkasına 55" menü ekranı asılır.

LOGO VE DAİRE TABELA (MHC Mola, arkadan LED)

· Ön siyah bantın ortasına MHC Mola logosu, kanal harf: 1302 geniş, 460 yüksek.
· Sol yan bantta aynı logo, 736 × 260.
· Sol yanda dışarı çıkan daire tabela: Ø720, 60 kalın, iki yüzü yazılı.
  Duvardan 120 mm dışarıda, ön köşeye 800 mm, ortası +2620.

TAVAN VE KLİMA

· İç tavan +2500. Üstündeki boşluğa gizli kanallı klima girer.
· Tavanda 60×60 bakım kapağı bırakılır. Dış ünite çatıda.

MHC Mola · Kiosk
5.0 × 3.0 × 3.0 m · prefabrik kahve kioskusu

PANEL · ÇITA · ALÜKOBOND · CAM

Tüm ölçüler mm'dir. Ölçüler sahada kontrol edilmeden imalata başlanmaz.

PAFTA 3/3
ÖLÇEK 1:5 · 1:20
TARİH 28.10.2026